
GAMBAR 1 - TAMPAK SAMPING RANGKA BAJA L = 60 m (STA 0+750) - KODE FRAME

Proyek FEED Road-4 PT Sumber Daya Arindo | Mutu baja SM490YB | Profil WB custom (pelat stok Indonesia)

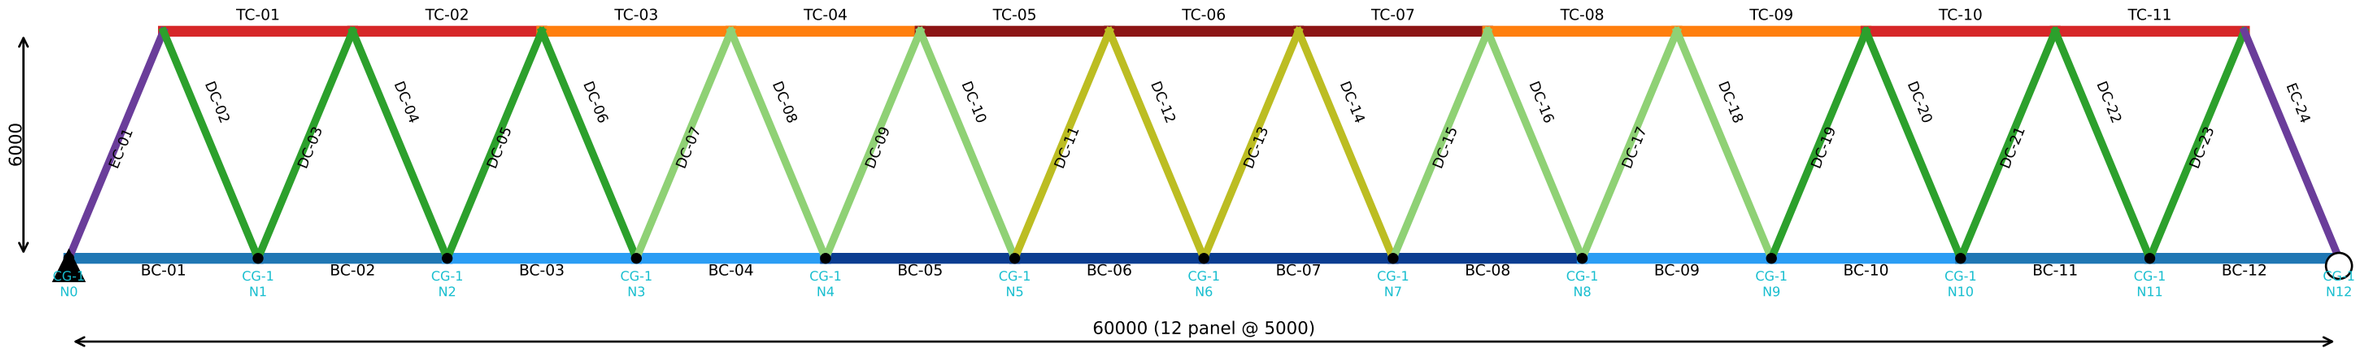


- BC-Z1 WB 500x250x22x22 (165.1 kg/m, UR 0.95)
- BC-Z2 WB 500x400x22x36 (300.0 kg/m, UR 0.95)
- BC-Z3 WB 500x500x14x40 (360.2 kg/m, UR 0.95)
- TC-Z1 WB 500x500x16x19 (207.2 kg/m, UR 0.94)
- TC-Z2 WB 500x475x16x36 (322.2 kg/m, UR 0.95)
- TC-Z3 WB 500x500x12x40 (353.6 kg/m, UR 0.95)
- EC-E WB 500x425x14x20 (184.0 kg/m, UR 0.92)
- DC-Z1 WB 500x400x16x16 (159.3 kg/m, UR 0.95)
- DC-Z2 WB 500x325x14x16 (133.1 kg/m, UR 0.88)
- DC-Z3 WB 500x275x14x16 (120.5 kg/m, UR 0.58)
- CG-1 WB 1350x350x10x22 (223.4 kg/m, UR 0.95)


GAMBAR 2 - DENAH IKATAN ANGIN ATAS & SISTEM LANTAI (BAWAH) - KODE FRAME

Proyek FEED Road-4 PT Sumber Daya Arindo | Mutu baja SM490YB | Profil WB custom (pelat stok Indonesia)

Denah Ikatan Angin Atas (Top Lateral)

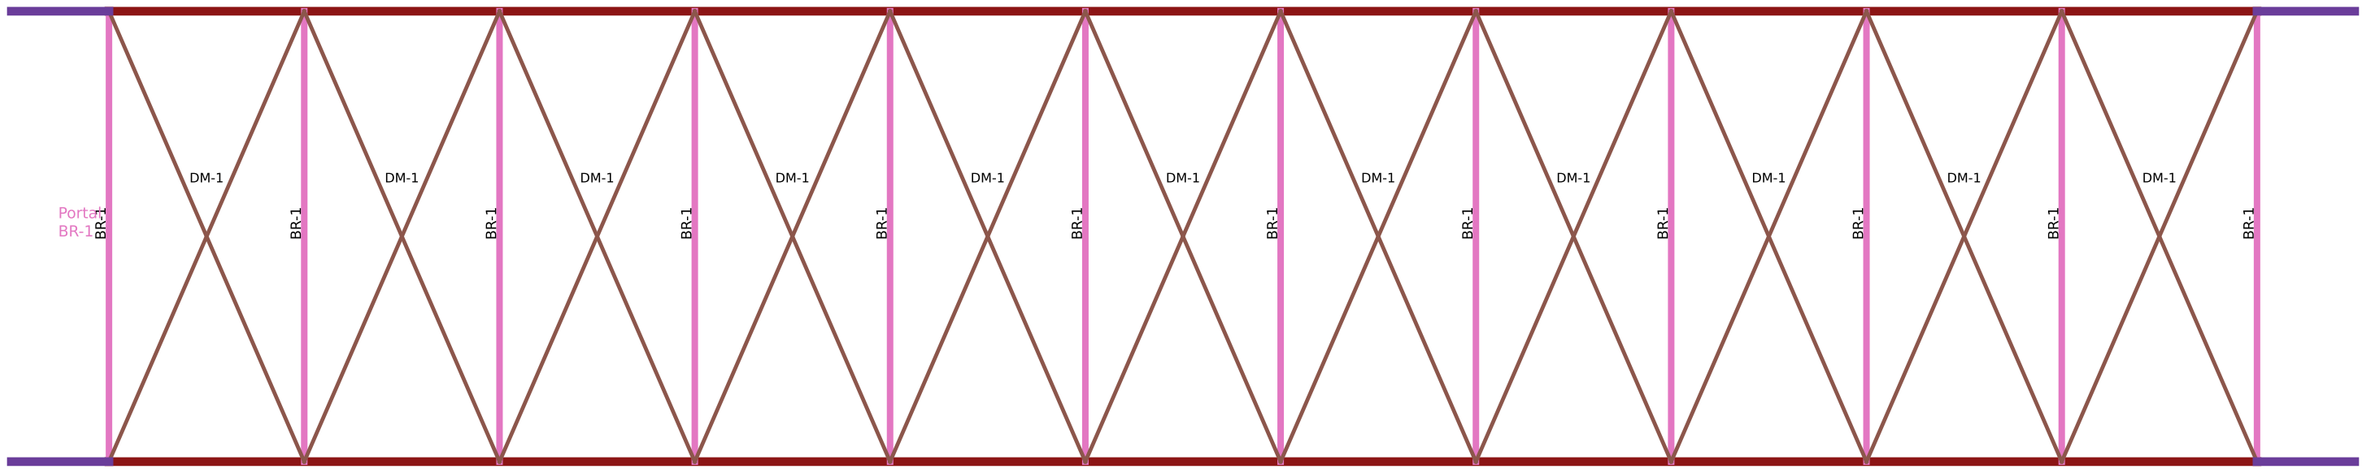


Denah Sistem Lantai & Ikatan Angin Bawah (Bottom Lateral)

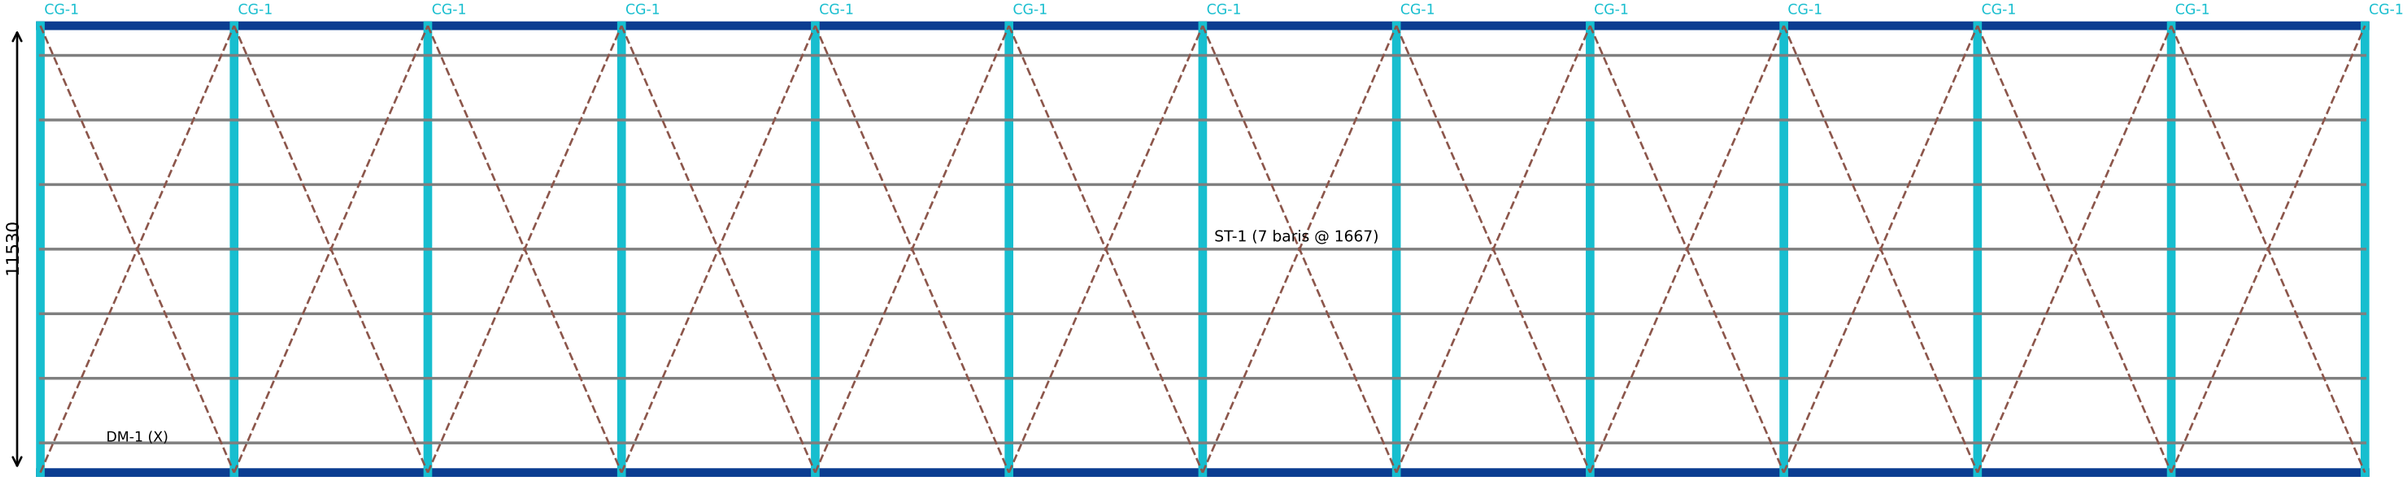

BR-1 WB 250x325x8x14 (85.4 kg/m, UR 0.26)
DM-1 WB 200x200x8x9 (39.7 kg/m, UR 0.57)
CG-1 WB 1350x350x10x22 (223.4 kg/m, UR 0.95)
ST-1 WB 550x225x9x14 (86.3 kg/m, UR 0.9)

GAMBAR 3 - POTONGAN MELINTANG RANGKA (PORTAL / TENGAH BENTANG) - KODE FRAME


Proyek FEED Road-4 PT Sumber Daya Arindo | Mutu baja SM490YB | Profil WB custom (pelat stok Indonesia)

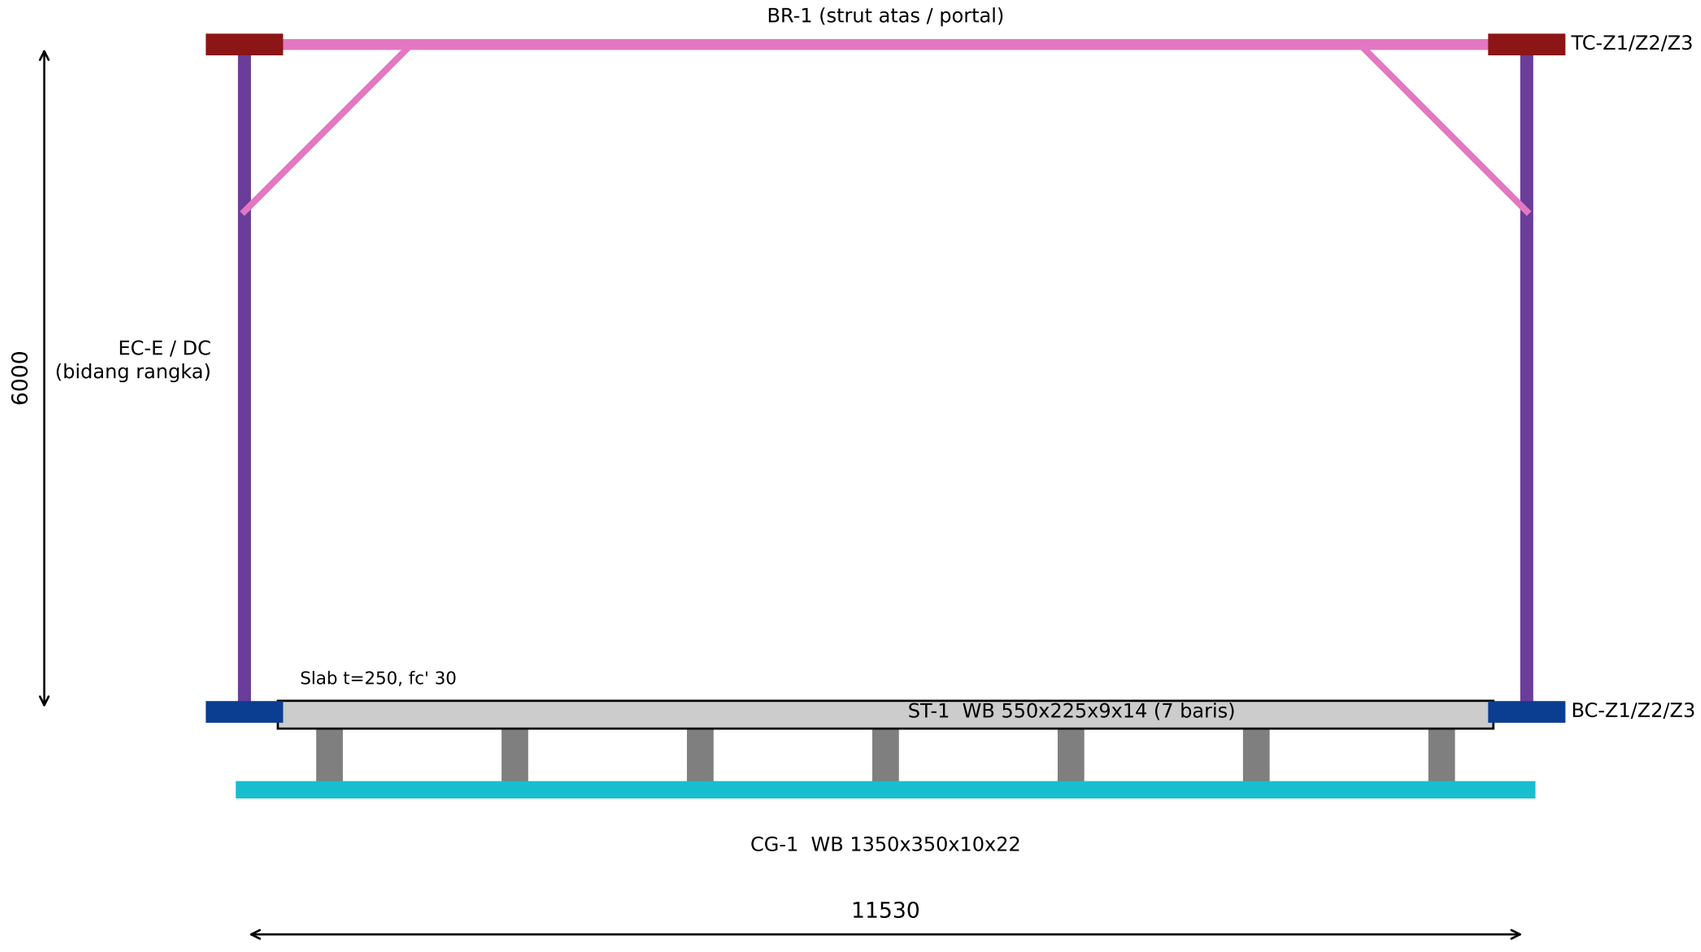


GAMBAR 4 - FLY OVER GIRDER KOMPOSIT L = 30.6 m (STA 0+050) - KODE FRAME

Proyek FEED Road-4 PT Sumber Daya Arindo | Mutu baja SM490YB | Profil WB custom (pelat stok Indonesia)

Denah Girder, Diafragma & Ikatan Angin Bawah

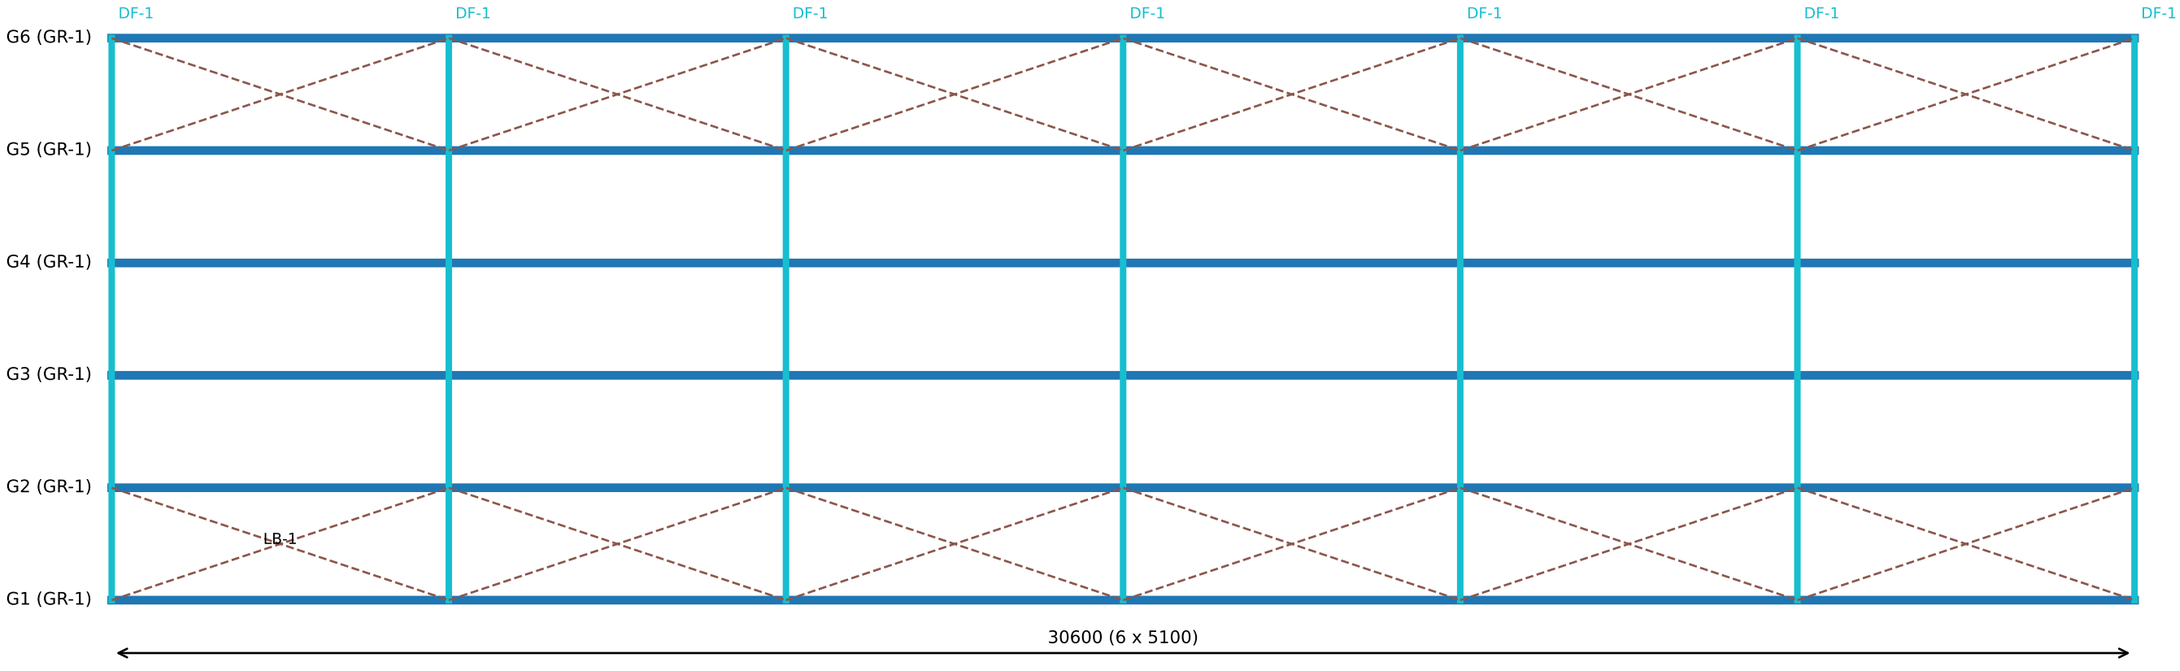

Potongan Melintang

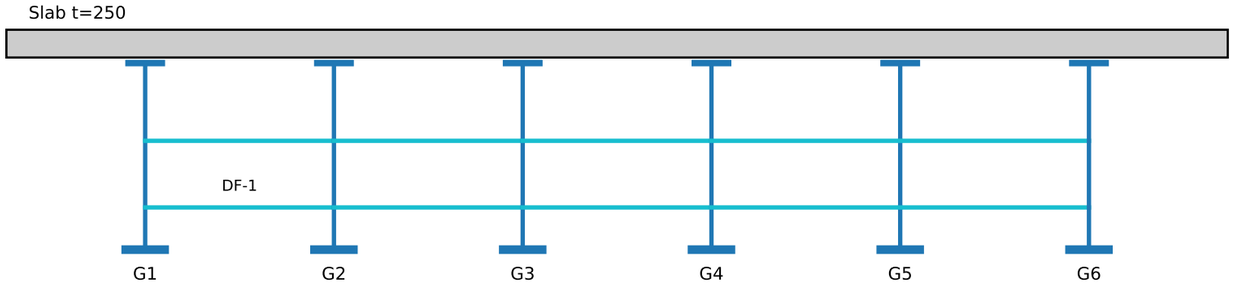


GR-1 WB 1700x300/350x12x16/20 (249.4 kg/m, UR 0.95)
DF-1 WB 600x200x9x12 (78.4 kg/m, UR 0.21)
LB-1 WB 200x200x8x12 (48.7 kg/m, UR 0.3)

GAMBAR 5 - DETAIL PENAMPANG WB (skala relatif, satuan mm)


Proyek FEED Road-4 PT Sumber Daya Arindo | Mutu baja SM490YB | Profil WB custom (pelat stok Indonesia)

BC-Z1
WB 500x250x22x22

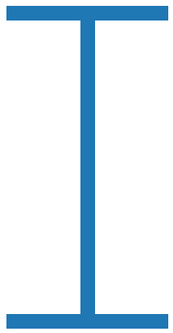

Bottom Chord
165.1 kg/m

BC-Z2
WB 500x400x22x36

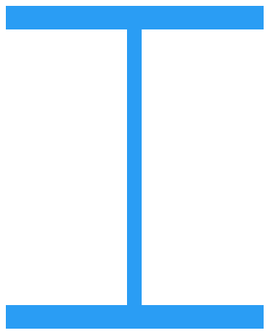


Bottom Chord
300.0 kg/m

BC-Z3
WB 500x500x14x40




Bottom Chord
360.2 kg/m

TC-Z1
WB 500x500x16x19

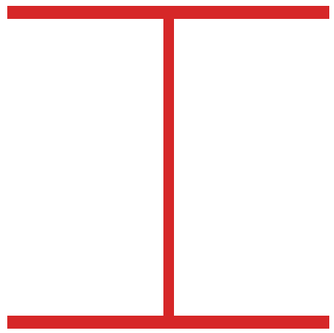


Top Chord
207.2 kg/m

TC-Z2
WB 500x475x16x36

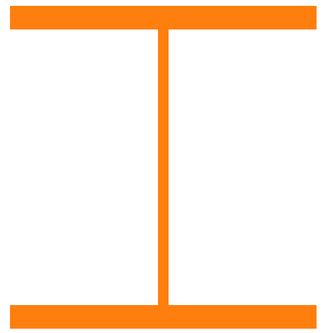


Top Chord
322.2 kg/m

TC-Z3
WB 500x500x12x40

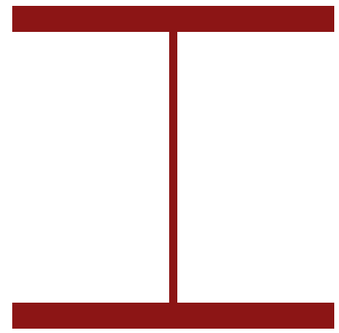


Top Chord
353.6 kg/m

EC-E
WB 500x425x14x20

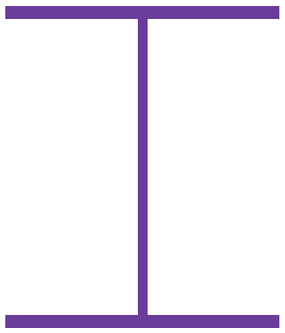


End Chord
184.0 kg/m

DC-Z1
WB 500x400x16x16

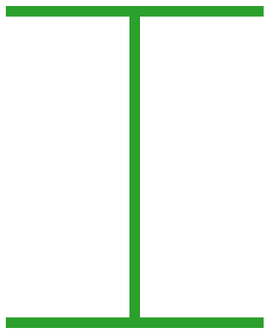


Diagonal Chord
159.3 kg/m

DC-Z2
WB 500x325x14x16

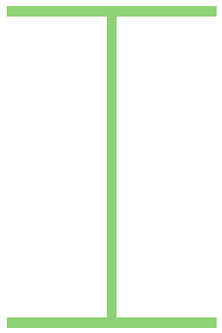

Diagonal Chord
133.1 kg/m

DC-Z3
WB 500x275x14x16

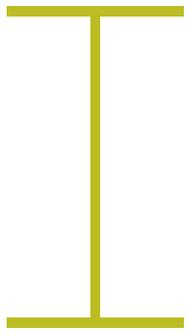

Diagonal Chord
120.5 kg/m

ST-1
WB 550x225x9x14




Stringer
86.3 kg/m

CG-1
WB 1350x350x10x22




Cross Girder
223.4 kg/m

BR-1
WB 250x325x8x14

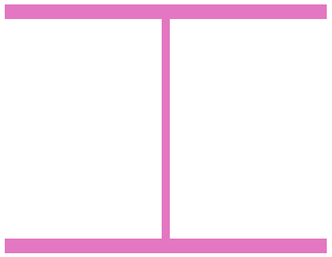

Brace (top lateral strut / por
85.4 kg/m

DM-1
WB 200x200x8x9

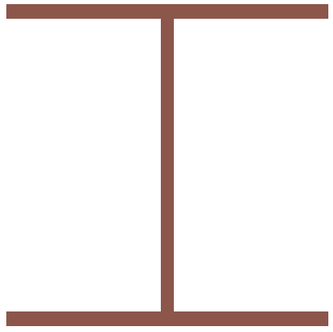


Diagonal Member (lateral X-bra
39.7 kg/m

GR-1
WB 1700x300/350x12x16/20




Main Girder (composite, interi
249.4 kg/m

DF-1
WB 600x200x9x12

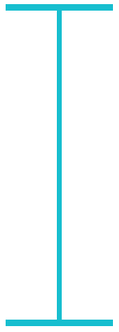

Diaphragm / Cross Beam
78.4 kg/m

LB-1
WB 200x200x8x12

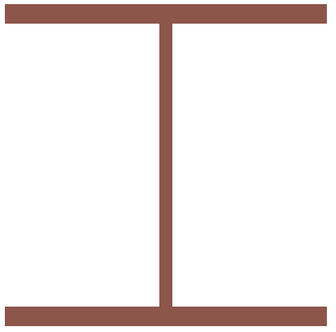

Lateral Bracing (erection)
48.7 kg/m